CONCEPTUAL LAND PLAN · DRAFT FOR DISCUSSION

Palo Blanco Ranch


±1,473 acres · South of Mangana-Hein Rd, Laredo / Webb County, Texas

1,473 ac	±1,026 ac	±340 ac	±107 ac
GROSS SITE	NET DEVELOPABLE	OPEN SPACE (23%)	ROADWAY ROW

N

0 1,000 2,000 FT

APPROX. SCALE · OCTOBER 2026

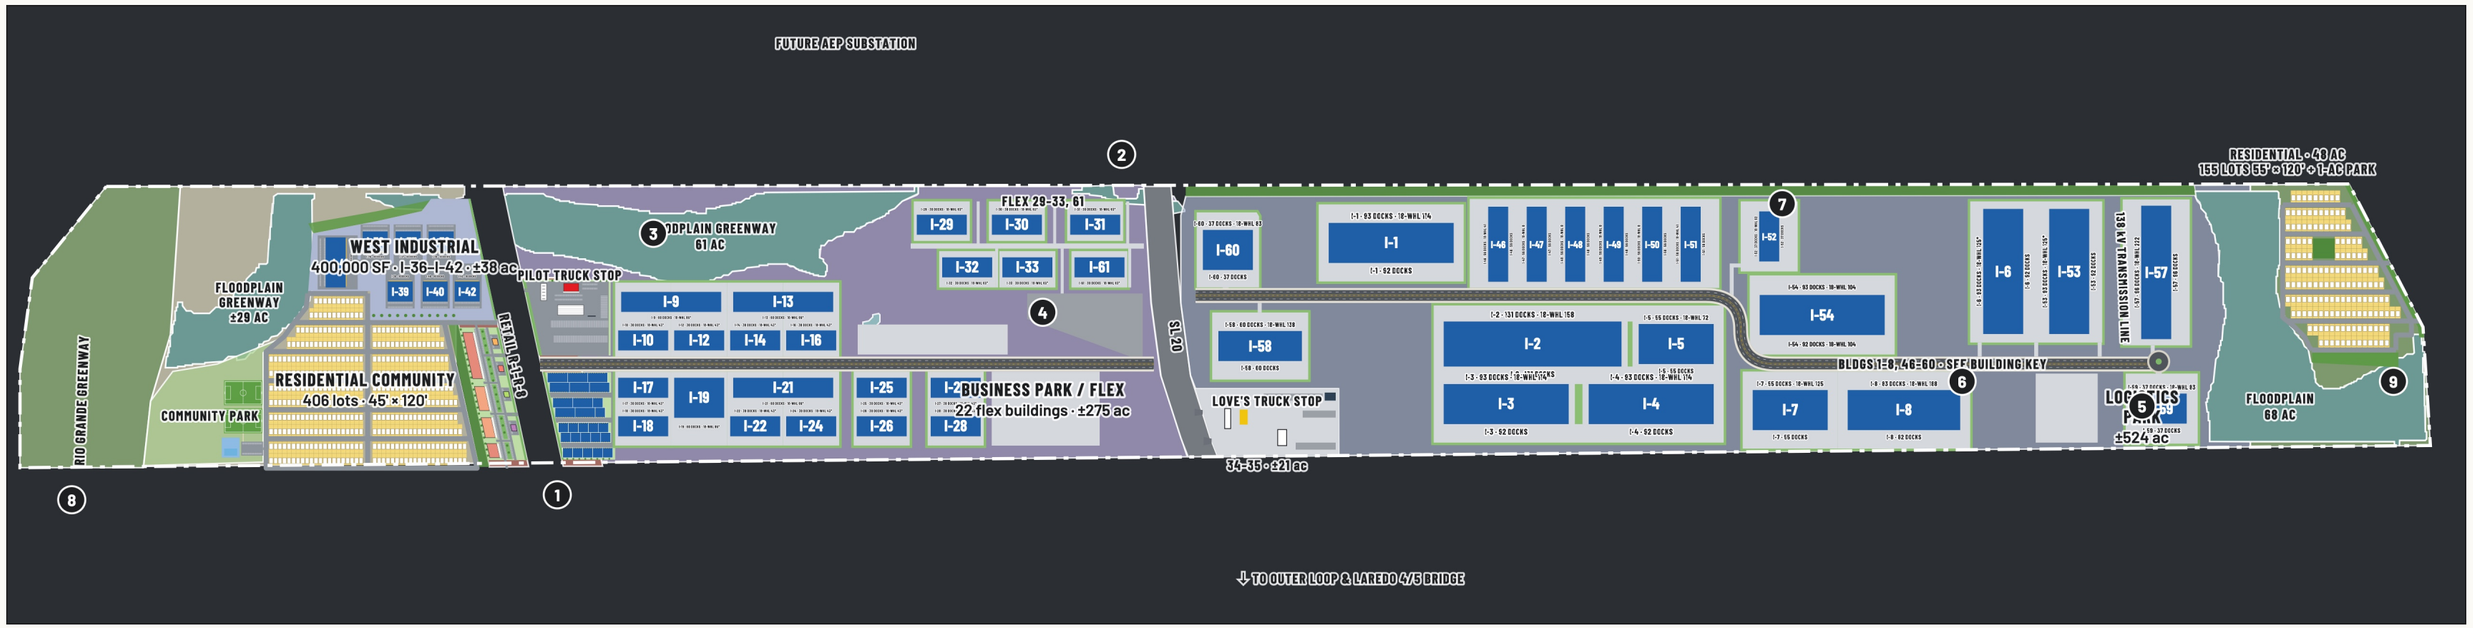

LAND USE SUMMARY

USE	ACRES	%
Residential community – 406 lots + clubhouse (incl. community park & buffer)	103	7.0
West industrial – 400,000 SF on US 83 (I-36–I-42)	38	2.6
Retail – US 83 frontage, west (R-1–R-8, 119,200 SF) + hwy commercial east	30	2.0
Love's truck stop (proposed) – SL 20 south node	21	1.4
Residential – 155 lots, 55' × 120' + 1-ac park & green space (Mangana-Hein)	48	3.3
Business park – 49 flex buildings, 2.97M SF + truck lots	270	18.3
Logistics park – 21 cross-docks (6.85M SF) + trailer storage lots	516	35.0
Rio Grande greenway & border corridor	82	5.6
Floodplain greenways, creek, pipeline trail & buffers	258	17.5
Roadway ROW (US 83, SL 20, 150' through roads)	107	7.3
Total	**1,473**	**100**

LEGEND

- Site boundary (±1,473 ac)
- 100' vegetated buffer
- Floodplain greenway / detention
- Through road / truck route · 150' ROW, 4 lanes + center two-way left-turn lane
- Future connection / floodplain crossing

Base aerial layers (your GIS): red dashed = pipelines, teal fill = 100-yr floodplain, blue dotted = 138 kV transmission line, pink dotted = city limits, white band = TxDOT SL 20 schematic, orange = Outer Loop / 4-5 Bridge.

KEY NOTES

1. Truck court labels (in the gray space beside each building): **DOCKS** = dock doors on that side, **18-WHL** = 18-wheeler / trailer stalls. Guest (car) parking counts are listed in the Building Key. * includes the building's share of a shared trailer lot: P2/P3 (43 per 100K, 86 per 200K bldg, Bldgs 9–28), P4 (63 each, 29–33 & 61), P1 (125 each, Bldgs 6 & 53). Each industrial site has a 25' landscaped green strip around its paving.
2. **US 83 frontage** – highway commercial both sides; a 100' vegetated buffer screens the residential community.
3. **SL 20 / Cuatro Vientos** (TxDOT preliminary) bisects the site; the former town center at CR 6073A is now part of the logistics park.
4. **Floodplain** along the north edge, the west flow path and the east end kept as greenway + regional detention; no lots in the 100-yr floodplain.
5. **Main pipeline** kept as a linear trail; confirm operators, easement widths and crossings.
6. **Existing 138 kV transmission line** runs north–south between Bldg 6 and the east floodplain; future AEP Mangana Hein substation north of the site.
7. **Creek corridor** through the logistics park kept as an open drainage greenway.
8. **La Presa colonia** – 100' landscape buffer along CR 6073A screens the logistics park; no truck access onto CR 6073A.
9. **Rio Grande / border corridor** (67-ac strip) – riverfront greenway; coordinate with CBP / IBWC.
10. **Logistics road ends in a cul-de-sac** between I-57 and I-59; the east floodplain crossing to Mangana-Hein Rd was removed, so no truck traffic passes the 155-lot neighborhood.

Conceptual only, drawn over the supplied GIS aerial (scale ≈ 24.6 ft/px). Oil & gas well sites per the RRC map are not shown; confirm status and setbacks before platting. Acreages are planning estimates; verify with survey, title and engineering.